

JOANNE MARK PORTFOLIO

Community Gardeners –
families are able to create their
own gardens in front of their houses.



Grant Fields

open area for families and neighboring visitors to enjoy the outdoors. multiple activities can be enjoyed such as picnicking, playing sports, taking in river views, etc.

Residential Housing

two-story, single family homes that includes backyard and garage, located in groups of six, eight, and ten.

Commercial Strip contains local grocery stores, coffee shops, pharmacy, local meat stores meant to be walking for grocery store entrance of the street small parking lot is the street. j. l. mark strip to provide a be surrounded by walkable for neig

Walking paths

these paths are located along the back of every house. they are meant to be strolling paths that people can walk along for exercise or a breath of fresh air. the paths are behind neighboring homes to encourage community but also is far away enough to allow privacy.

J. L. Mark Square

a relaxing resting area for people who have been busy shopping or walking around the commercial area; located in two different parts. it is also the main corridor for the residents to get from one side to the other through a serene garden. many bushes and flowers are planted to reduce echoing between buildings and create a natural scenery for people.

Clara Commons


bbq area and kids playground. (can be called the Clara commons) in other words encourages people to gather in the bbq area for families to interact with each other.

Entourage	1
Revit	2-3
Sketch Up	4-6
Hand Draft & Modeling	7
AutoCad	8-9
Resume	10

CONTENTS



ENTOURAGE

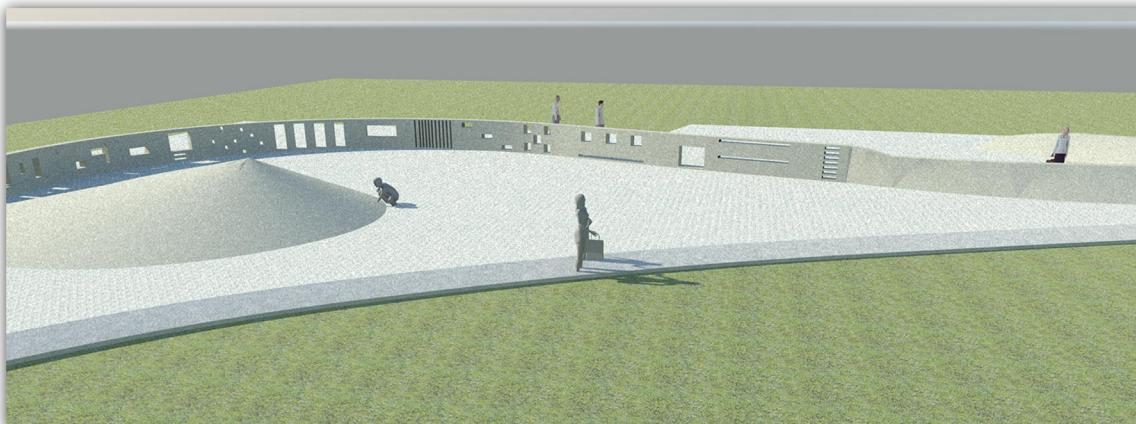

REVIT





REVIT





SKETCH UP




SKETCH UP

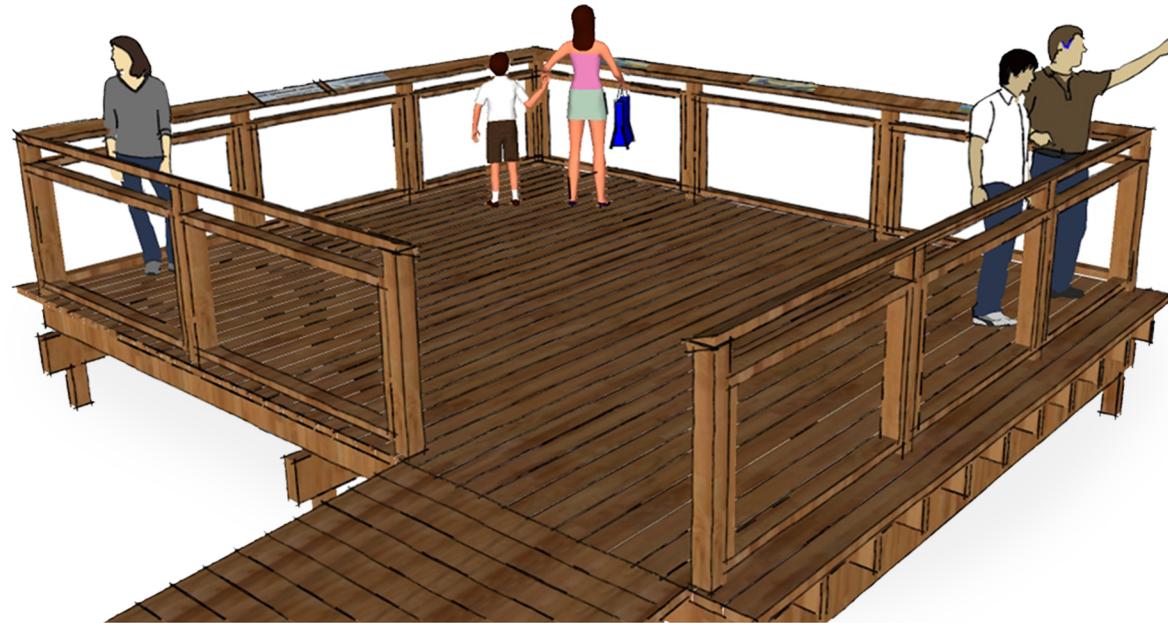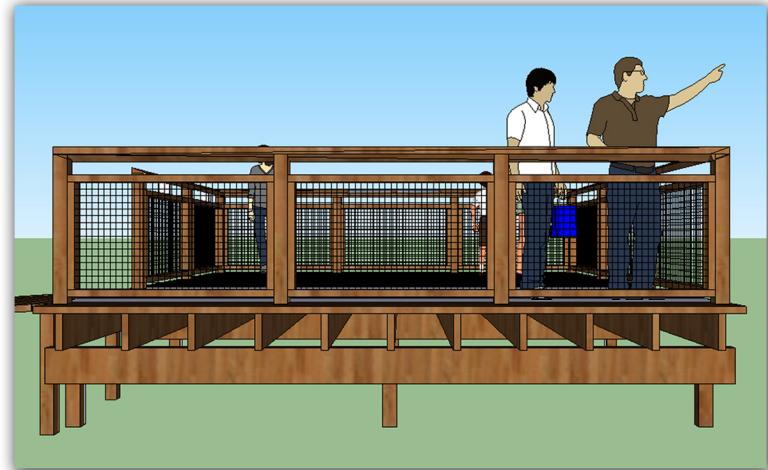



SKETCH UP

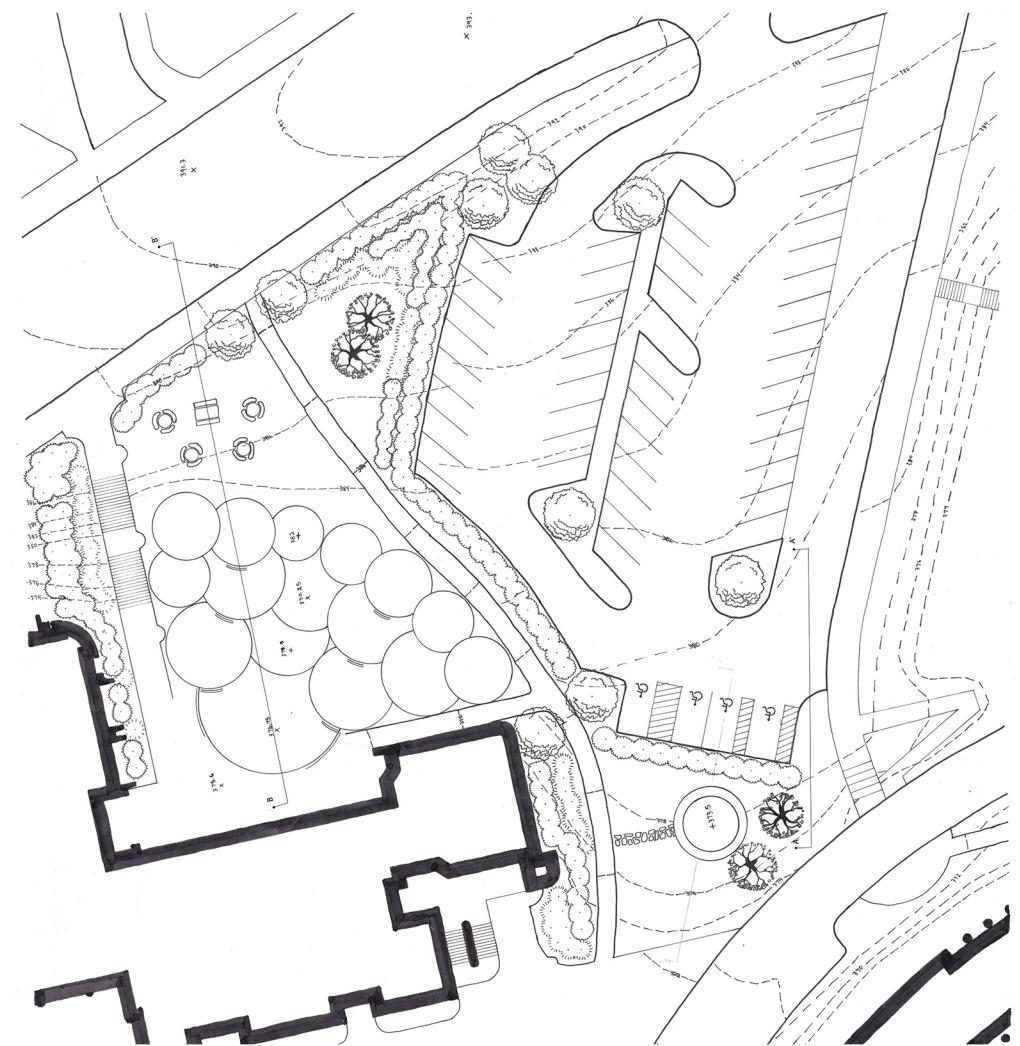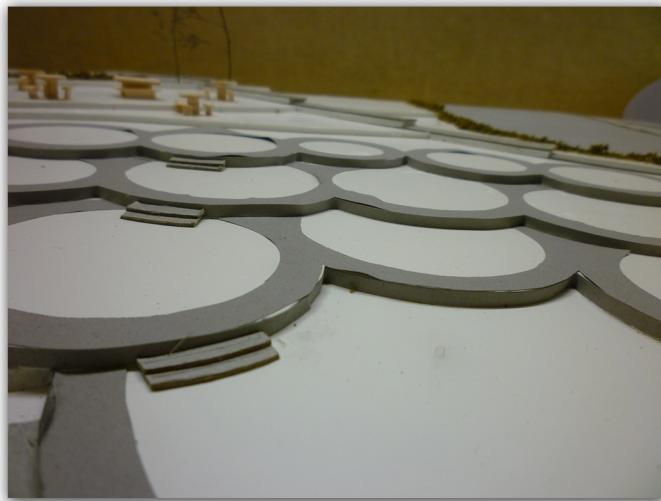

HAND DRAFT & MODELING

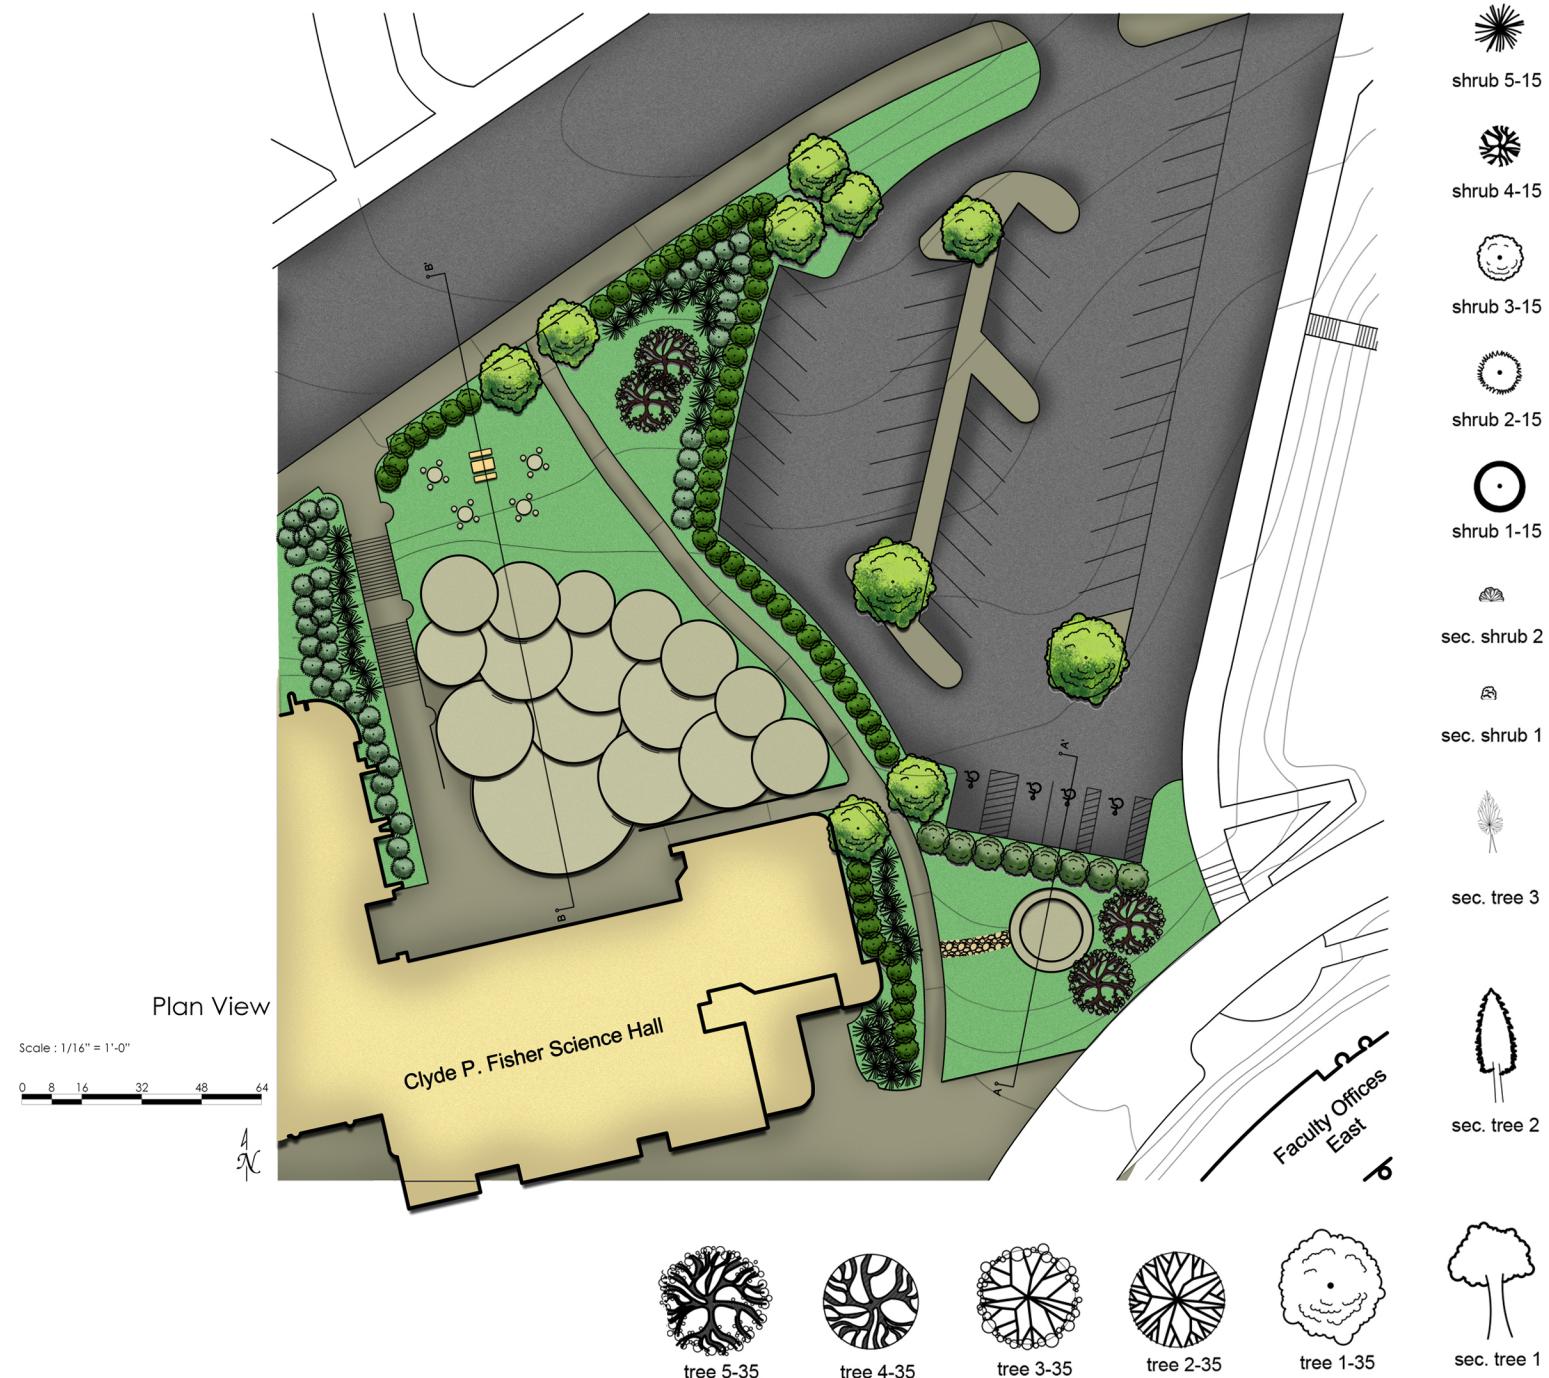

AUTOCAD

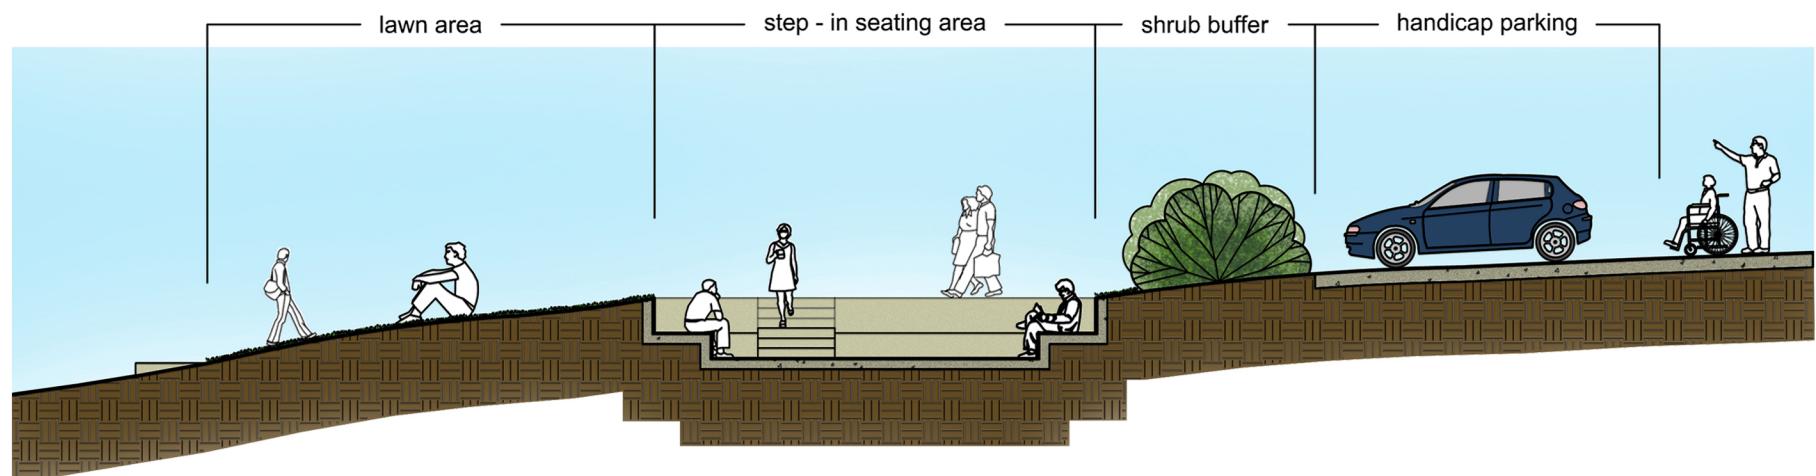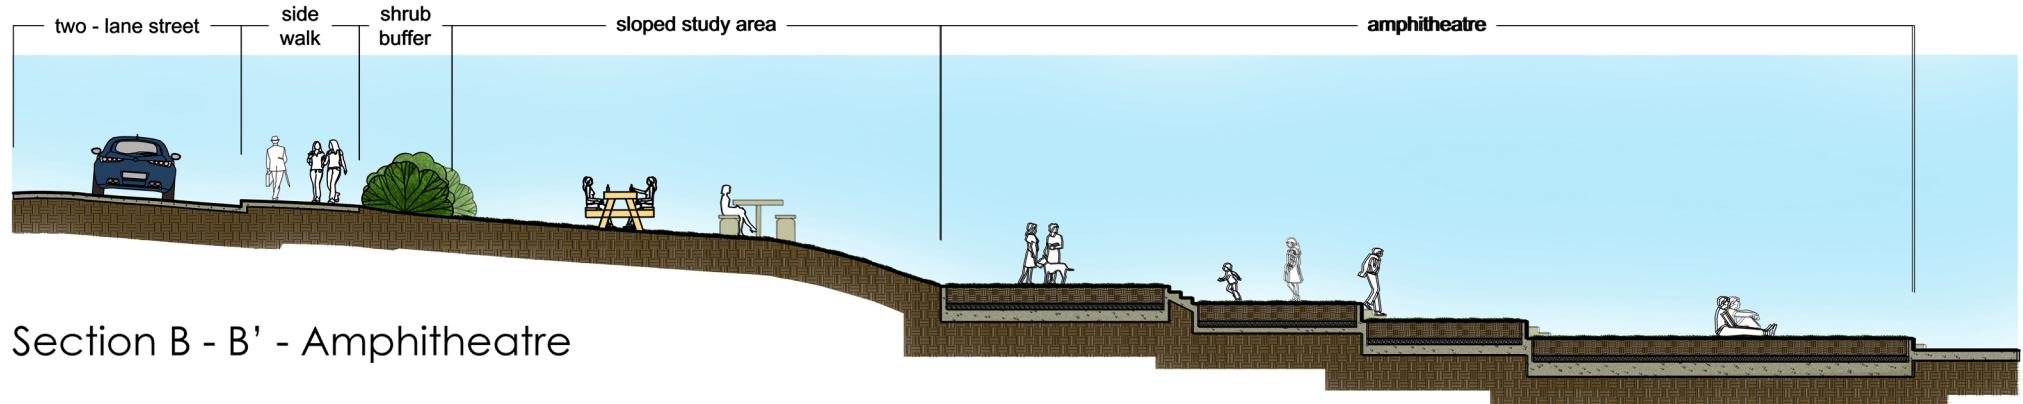

Scale : 1/8" = 1'-0"



AUTOCAD

EDUCATION

California Polytechnic State University, San Luis Obispo, CA 93410, BLA - Anticipated Graduation 2014

**SKILLS**

Fluent in Chinese and English

Computer Experience in Revit, AutoCAD, SketchUp, Adobe Photoshop, Adobe Illustrator, and Adobe InDesign

Great organizational skills and attention to detail

WORK EXPERIENCE**CALIFORNIA POLYTECHNIC STATE UNIVERSITY DISTRIBUTION CENTER: APRIL 2012 - PRESENT**

On campus: Responsibilities include process shipping orders, re-stocking inventory, and other hands-on tasks needed in preparation for Open House weekend.

PILOT PROFESSIONAL SHADOW PROGRAM FOR LANDSCAPE ARCHITECTURE MAJORS: JULY 2009

Located in San Francisco: Participation included time spent with Landscape Architecture firms PWP Landscape Architecture, SWA Group, and CMG Landscape Architecture to gain knowledge of real world work experience in landscape architecture.

VISITACION VALLEY GREENWAY PROJECT: JUNE 2005 - SEPTEMBER 2009

Located in San Francisco: Founding member duties include: planting, weeding, and watering plants in local community gardens, and maintenance of community gardens and parks.

COMMUNITY INVOLVEMENT**INTERVARSITY CHRISTIAN FELLOWSHIP: SEPTEMBER 2011 – PRESENT**

Asian American Ministry Leader: Responsibilities include establishing the Cal Poly chapter, building a community for Asian Americans to explore culture and see what it looks like to follow Jesus, and supporting the larger organization of InterVarsity with events and meetings.

SCIENCE CLUB PHILLIP AND SALA BURTON ACADEMIC HIGH SCHOOL: SEPTEMBER 2006 – SEPTEMBER 2008

Club Officer: Responsibilities include organizing field trips and school events, overlooking and assisting in events, and taking attendance.

ACTIVITIES

Computing, reading, hiking, volleyball, glowstringing, spending time in community, playing board games, camping

RESUME

Jun Hyun Kim, Ph.D.
Assistant Professor
Dept. of Landscape Arch. and Urban Planning
College of Architecture
Texas A&M University
318A Langford BLDG A.
College Station, TX 77843-3137
Email: jhkim@arch.tamu.edu
Tel: 979-845-2532 / Fax: 979-862-1784

Fram Martin
Co-founder of Visitacion Valley Greenway
Project
186 Arleta Ave
San Francisc, CA 94134
(415) 468-0639
fran@visvalleygreenway.org

REFERENCES